

BLOCK- A

<p>NOTES:</p> <ol style="list-style-type: none"> all dimensions and levels are in feet and inches, unless otherwise mentioned. dimensions are not to be scaled. only written dimensions are to be followed. this drawing shall be read in conjunction with relevant architectural, structural and electrical drawings and all relevant sections of the specifications, if applicable. any discrepancy, error or ambiguity shall be immediately brought to the notice of the architect before the commencement of work. this drawing shall supersede its previous revisions. all rcc works shall be done in accordance with structural drawings. 						<p>CLIENT: M/S. VIRAAJ & V.H.R BUILDERS</p> <p>PROJECT: Prop. Residential Flats @ Gudlapochampalli (Proposal for C + 3 S + 15 + 2 Floors)</p> <p>TITLE: SKETCH PLAN (BLOCK-A)</p>	<p>JOB NO:</p> <table border="1"> <tr><td>DRAWN:</td><td>KHAJA</td></tr> <tr><td>REVISED:</td><td></td></tr> <tr><td>CHECKED:</td><td>H.V</td></tr> <tr><td>APPROVED:</td><td>V.V</td></tr> <tr><td>DATE:</td><td>03-03-2023</td></tr> </table> <p>DRG. No: V V A </p> <p>REV R 0</p>	DRAWN:	KHAJA	REVISED:		CHECKED:	H.V	APPROVED:	V.V	DATE:	03-03-2023	<p>RELEASED FOR</p> <table border="1"> <tr><td><input type="checkbox"/> INFORMATION</td></tr> <tr><td><input type="checkbox"/> TENTATIVE</td></tr> <tr><td><input checked="" type="checkbox"/> REVIEW</td></tr> <tr><td><input type="checkbox"/> CONSTRUCTION</td></tr> <tr><td><input type="checkbox"/> ASBUILT</td></tr> </table>	<input type="checkbox"/> INFORMATION	<input type="checkbox"/> TENTATIVE	<input checked="" type="checkbox"/> REVIEW	<input type="checkbox"/> CONSTRUCTION	<input type="checkbox"/> ASBUILT	<p>NORTH</p> 	<p>CONSULTANT: V.V. ASSOCIATES ARCHITECTS, ENGINEERS & INTERIOR DESIGNERS V.V.S CREST, ROAD NO-4, BANJARA HILLS, HYDERABAD. PHONE: 23354222, 42024599 EMAIL ID: h_vardhan2008@yahoo.com</p>
DRAWN:	KHAJA																								
REVISED:																									
CHECKED:	H.V																								
APPROVED:	V.V																								
DATE:	03-03-2023																								
<input type="checkbox"/> INFORMATION																									
<input type="checkbox"/> TENTATIVE																									
<input checked="" type="checkbox"/> REVIEW																									
<input type="checkbox"/> CONSTRUCTION																									
<input type="checkbox"/> ASBUILT																									
Rev No.	DESCRIPTION OF REVISION	BY	DATE																						

© V.V.ASSOCIATES
 This document should not be relied on or used in circumstances other than those for which it was originally prepared and for which V.V. Associates was commissioned. V.V. Associates accepts no responsibility for this document to any other party other than the person by whom it was commissioned.

NOTES:


- all dimensions and levels are in feet and inches, unless otherwise mentioned.
- dimensions are not to be scaled, only written dimensions are to be followed.
- this drawing shall be read in conjunction with relevant architectural, structural and electrical drawings and all relevant sections of the specifications, if applicable.
- any discrepancy, error or ambiguity shall be immediately brought to the notice of the architect before the commencement of work.
- this drawing shall supersede its previous revisions.
- all rcc works shall be done in accordance with structural drawings.

Rev No.	DESCRIPTION OF REVISION	BY	DATE

CLIENT:
 M/S. VIRAJ & V.H.R BUILDERS

PROJECT:
 Prop. Residential Flats @ Gudlapochampalli
 (Proposal for C + 3 S + 15 + 2 Floors)

TITLE:
 SKETCH PLAN (BLOCK-B)

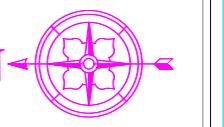RELEASED FOR	NORTH
<input type="checkbox"/> INFORMATION <input type="checkbox"/> TENTATIVE <input type="checkbox"/> REVIEW <input type="checkbox"/> CONSTRUCTION <input type="checkbox"/> ASBUILT	 SCALE : 1" : 8'-0"

JOB NO:
DEALT: KHAJA
DRAWN: XXXXXX
CHECKED: H.V
APPROVED: V.V
DATE: 03-03-2023

DRG. No:
 V V A

REV
 R 0

CONSULTANT:
V.V. ASSOCIATES
 ARCHITECTS, ENGINEERS & INTERIOR DESIGNERS
 V.V.S.CREST, ROAD NO-4,
 BANJARA HILLS, HYDERABAD.
 PHONE: 23354222, 42024599
 EMAIL ID: h_vardhan2008@yahoo.com



BLOCK- B

© V.V.ASSOCIATES
 This document should not be relied on or used in circumstances other than those for which it was originally prepared and for which V.V. Associates was commissioned. V.V. Associates accepts no responsibility for this document to any other party other than the person by whom it was commissioned.

NOTES:

- all dimensions and levels are in feet and inches, unless otherwise mentioned.
- dimensions are not to be scaled, only written dimensions are to be followed.
- this drawing shall be read in conjunction with relevant architectural, structural and electrical drawings and all relevant sections of the specifications, if applicable.
- any discrepancy, error or ambiguity shall be immediately brought to the notice of the architect before the commencement of work.
- this drawing shall supersede its previous revisions.
- all rcc works shall be done in accordance with structural drawings.

Rev No.	DESCRIPTION OF REVISION	BY	DATE

CLIENT:

M.S. VIRAJ & V.H.R BUILDERS

PROJECT:
 Prop. Residential Flats @ Gudlapochampalli
 (Proposal for C + 3 S + 15 + 2 Floors)

TITLE:
 SKETCH PLAN (BLOCK-C)


RELEASED FOR	NORTH
<input type="checkbox"/> INFORMATION	
<input type="checkbox"/> TENTATIVE	
<input type="checkbox"/> REVIEW	
<input type="checkbox"/> CONSTRUCTION	
<input type="checkbox"/> ASBUILT	

JOB NO:
DEALT: KHAJA
DRAWN: XXXXXX
CHECKED: H.V
APPROVED: V.V
DATE: 03-03-2023


DRG. No:
 V V A

REV
 R 0

CONSULTANT:
V.V. ASSOCIATES
 ARCHITECTS, ENGINEERS & INTERIOR DESIGNERS
 V.V.S.CREST, ROAD NO-4,
 BANJARA HILLS, HYDERABAD.
 PHONE: 23354222, 42024599
 EMAIL ID: h_vardhan2008@yahoo.com

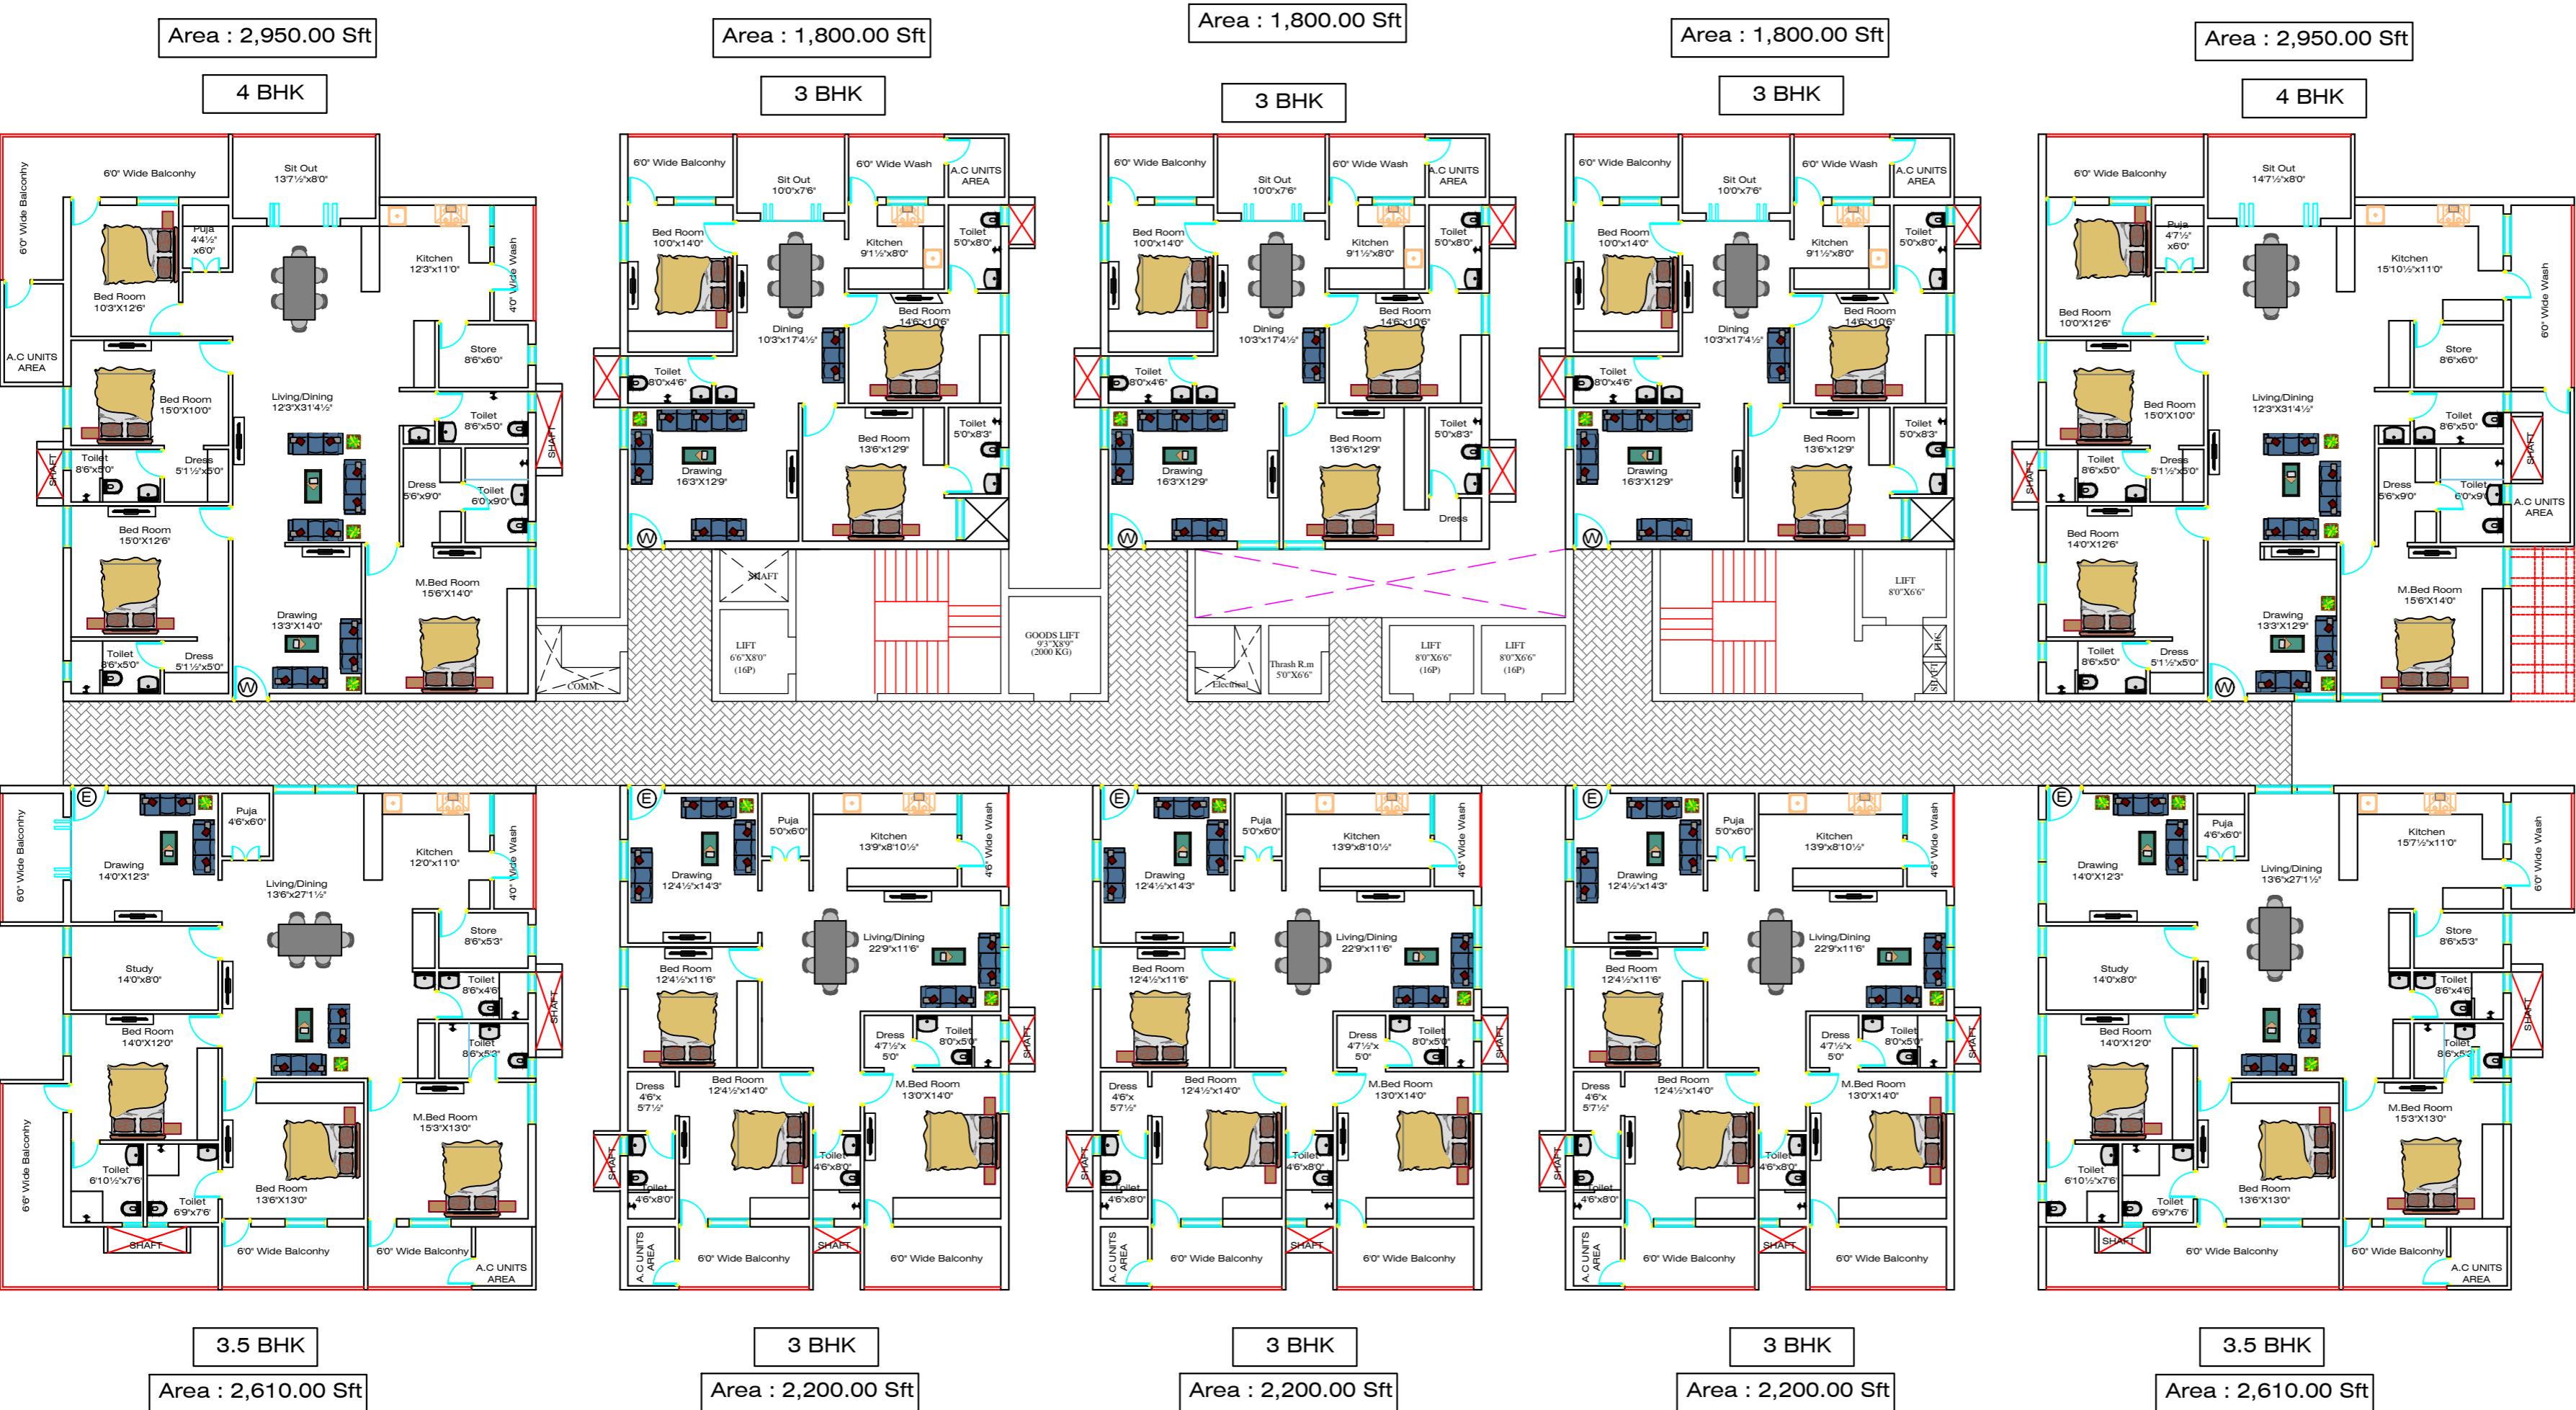

BLOCK- C

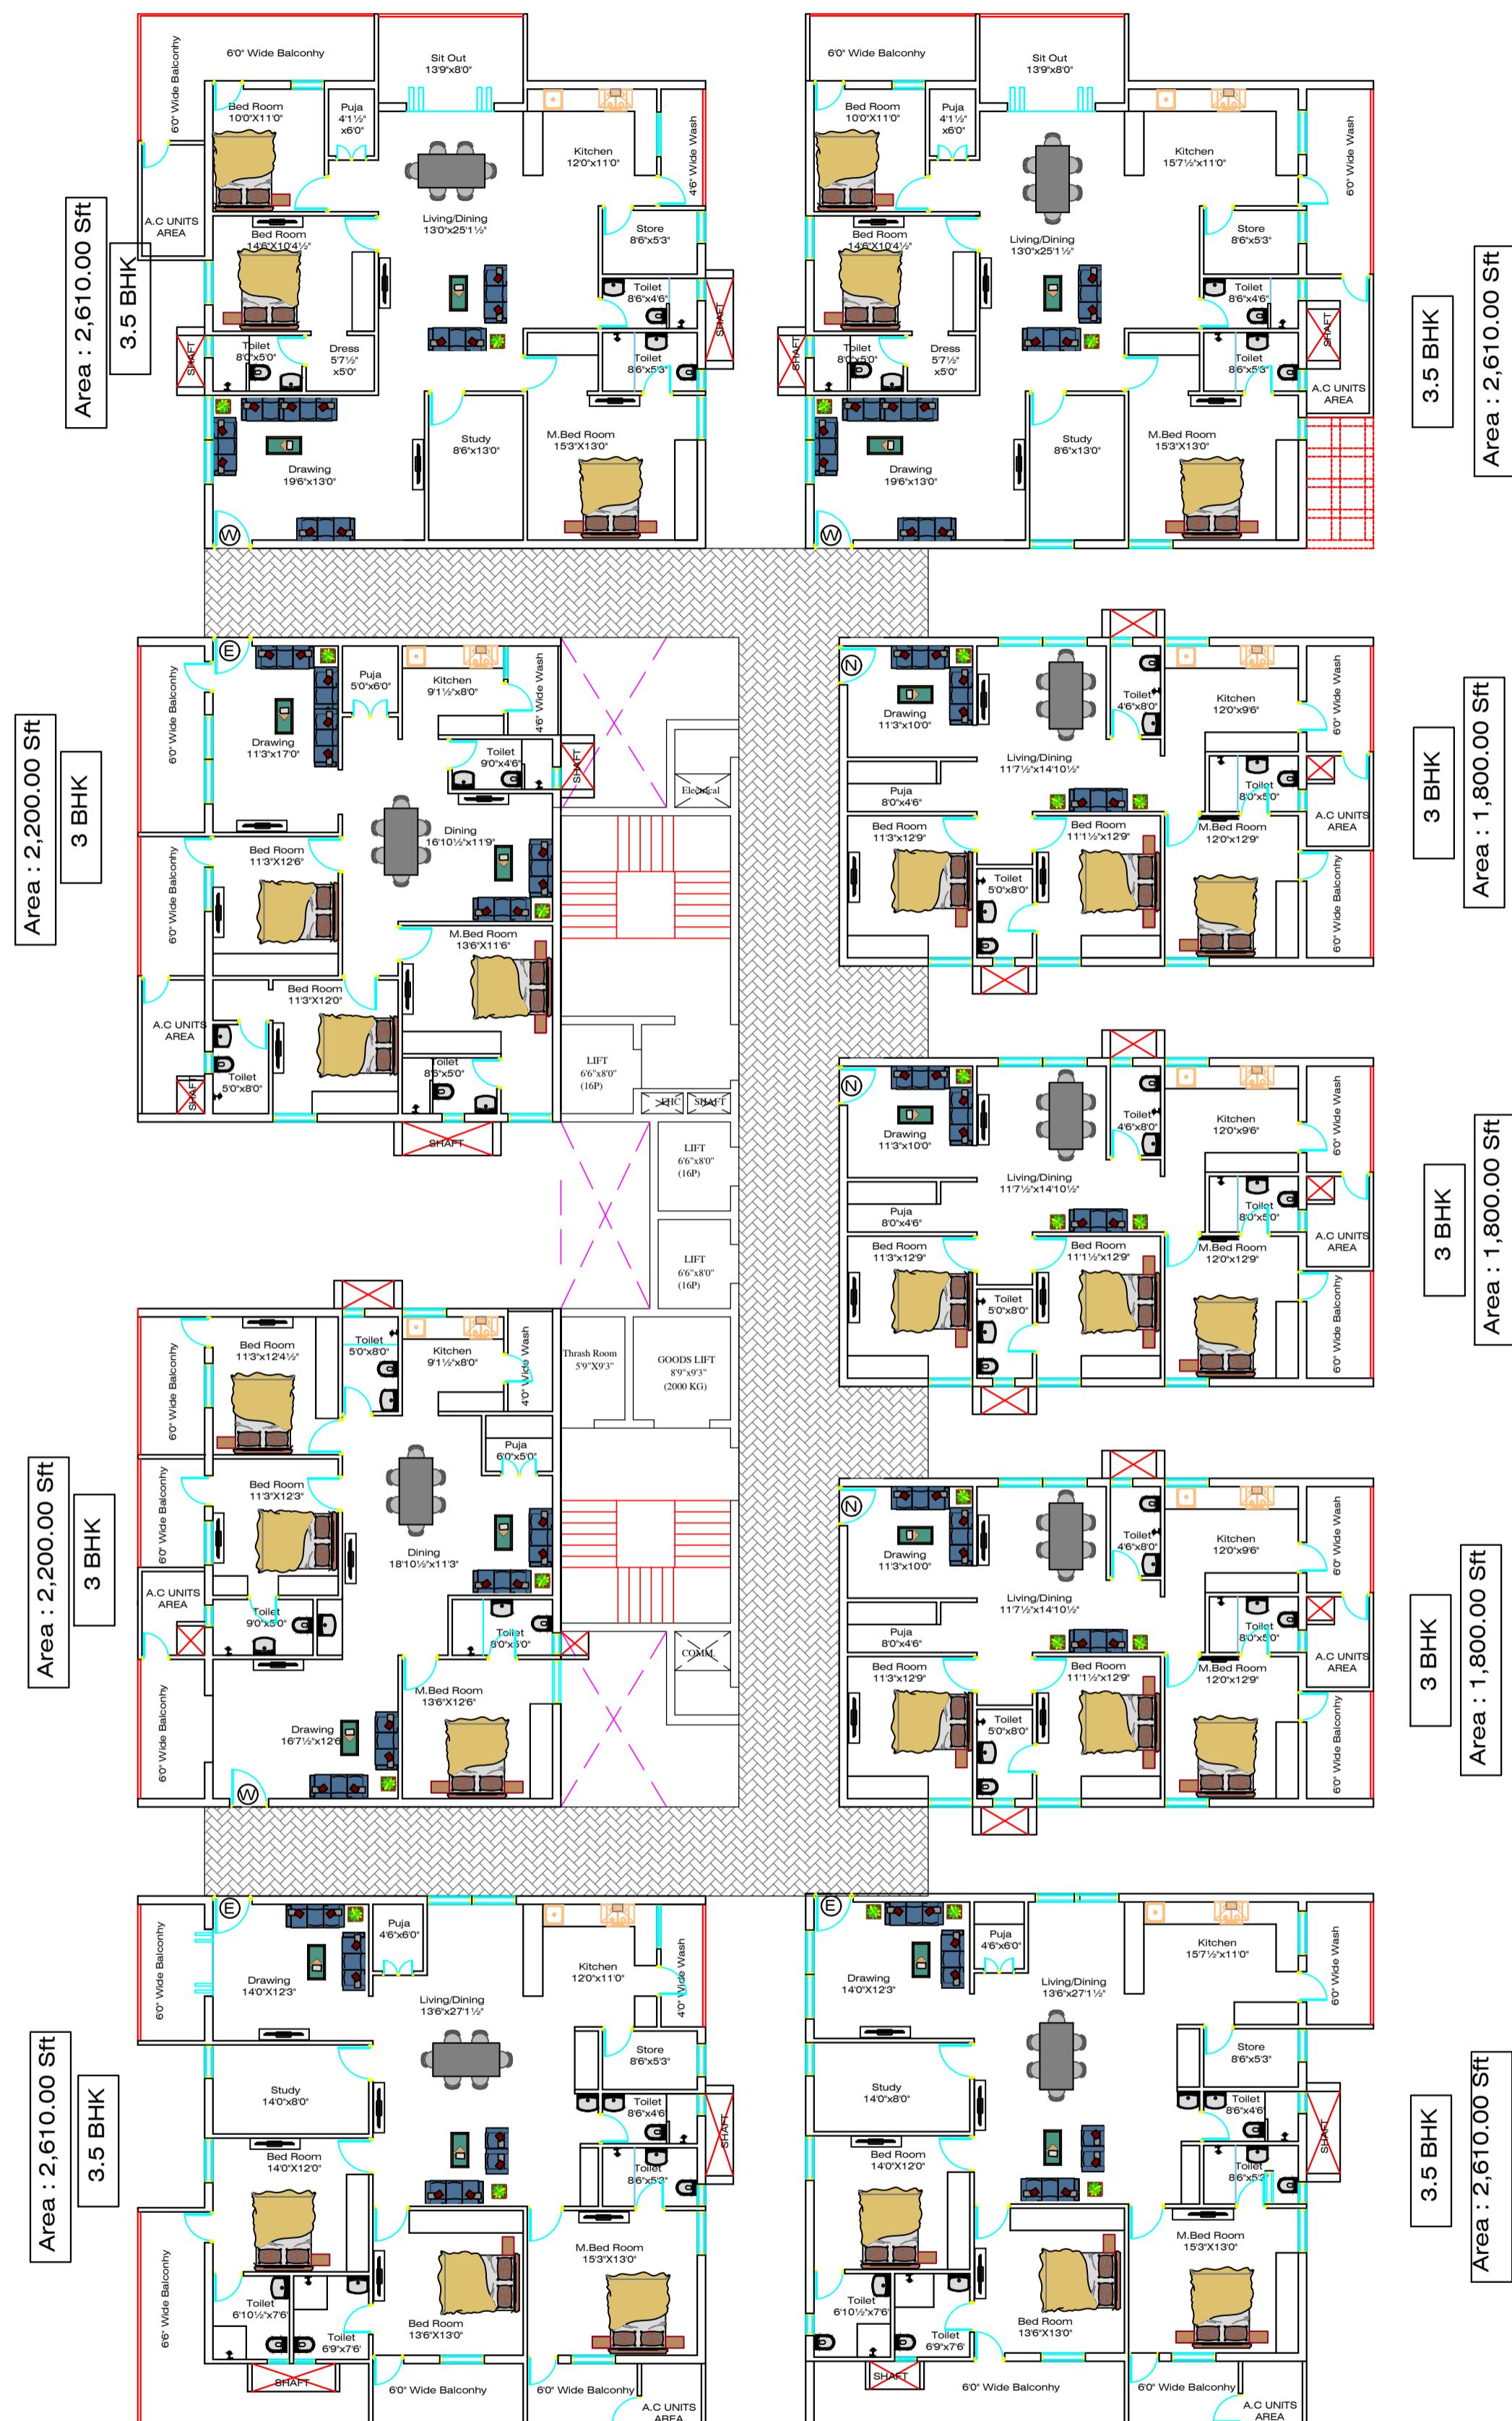

BLOCK- D

NOTES:

- all dimensions and levels are in feet and inches, unless otherwise mentioned.
- dimensions are not to be scaled, only written dimensions are to be followed.
- this drawing shall be read in conjunction with relevant architectural, structural and electrical drawings and all relevant sections of the specifications, if applicable.
- any discrepancy, error or ambiguity shall be immediately brought to the notice of the architect before the commencement of work.
- this drawing shall supersede its previous revisions.
- all rcc works shall be done in accordance with structural drawings.

Rev No.	DESCRIPTION OF REVISION	BY	DATE	CLIENT: M/S. VIRAAJ & V.H.R BUILDERS	JOB NO:	RELEASED FOR	NORTH
				PROJECT: Prop. Residential Flats @ Gudlapochampalli (Proposal for C + 3 S + 15 + 2 Floors)	DRAWN: KHAJA REVISED: HV CHECKED: HV APPROVED: V.V DATE: 03-03-2023	<input type="checkbox"/> INFORMATION <input type="checkbox"/> TENTATIVE <input checked="" type="checkbox"/> REVIEW <input type="checkbox"/> CONSTRUCTION <input type="checkbox"/> ASBUILT	
				TITLE: SKETCH PLAN (BLOCK-D)	DRG. No: V V A		
					REV R 0		
							© V.V.ASSOCIATES This document should not be relied on or used in circumstances other than those for which it was originally prepared and for which V.V. Associates was commissioned. V.V. Associates accepts no responsibility for this document to any other party other than the person by whom it was commissioned.
							CONSULTANT: V. V. ASSOCIATES ARCHITECTS, ENGINEERS & INTERIOR DESIGNERS V.V.S.CREST, ROAD NO.4 BANJARA HILLS, HYDERABAD, PHONE: 23354222, 42024599 EMAIL ID: h_vardhan2008@yahoo.com

© V.V.ASSOCIATES
 This document should not be relied on or used in circumstances other than those for which it was originally prepared and for which V.V. Associates was commissioned. V.V. Associates accepts no responsibility for this document to any other party other than the person by whom it was commissioned.

NOTES:

1. all dimensions and levels are in feet and inches, unless otherwise mentioned.
2. dimensions are not to be scaled, only written dimensions are to be followed.
3. this drawing shall be read in conjunction with relevant architectural, structural and electrical drawings and all relevant sections of the specifications, if applicable.
4. any discrepancy, error or ambiguity shall be immediately brought to the notice of the architect before the commencement of work.
5. this drawing shall supersede its previous revisions.
6. all rcc works shall be done in accordance with structural drawings.

Rev No.	DESCRIPTION OF REVISION	BY	DATE

CLIENT:
 M/S. VIRAJ & V.H.R BUILDERS

PROJECT:
 Prop. Residential Flats @ Gudlapochampalli
 (Proposal for C + 3 S + 15 + 2 Floors)

TITLE:
 SKETCH PLAN (BLOCK-E)

RELEASED FOR	NORTH
<input type="checkbox"/> INFORMATION <input type="checkbox"/> TENTATIVE <input type="checkbox"/> REVIEW <input type="checkbox"/> CONSTRUCTION <input type="checkbox"/> ASBUILT	
SCALE : 1" : 8'-0"	

JOB NO:
DEALT: KHAJA
DRAWN: XXXXXX
CHECKED: H.V
APPROVED: V.V
DATE: 04-03-2023

DRG. No:
 V V A

REV
 R 0

CONSULTANT:
V.V. ASSOCIATES
 ARCHITECTS, ENGINEERS & INTERIOR DESIGNERS
 V.V.S.CREST, ROAD NO-4,
 BANJARA HILLS, HYDERABAD.
 PHONE: 23354222, 42024599
 EMAIL ID: h_vardhan2008@yahoo.com

BLOCK- E

